



PLANNING &
DEVELOPMENT
2101 O'Neil Avenue
Cheyenne, WY 82001
(307) 637-6282
cheyennecity.org

MEMO

To: Honorable Mayor Patrick Collins and Members of the City Council
From: Connor White, Planner II
Subject: PUDC-26-50 / Harmony Valley, 23rd Filing – Expedited Plat
Date: May 11, 2026

Background:

The item for consideration is a Final Plat. This is approved by Resolution.

The proposed Governing Body review schedule is as follows:

- Introduction and Referral May 11, 2026
- Public Services Committee May 18, 2026
- Final Consideration May 26, 2026

Planning Commission Recommendation:

The Planning Commission heard this item at their May 4, 2026 meeting and recommended the Governing Body approve this application with the following exception and condition:

1. The following exceptions be granted:
 - a. Exceptions to block size for perimeter blocks due to topography and civic uses.
2. Prior to recording of the final plat:
 - a. A pedestrian access easement be provided connecting Medley Loop to Grand Harmony Blvd. If, after extensive engineering, the City Engineer determines a pedestrian connection is not feasible, the Director may waive or modify this condition.

The Planning Commission Staff report is attached and has not been changed.

Public Comment

As of the creation of this memo (May 6, 2026), Staff has received no inquires or comments from the public on this project. The project page on the website has received 136 views and no comments.

Attachments:

1. Resolution
2. Planning Commission Staff Report

RESOLUTION NO. _____

ENTITLED: "A RESOLUTION AUTHORIZING THE MAYOR AND THE CITY CLERK TO SIGN A FINAL PLAT FOR HARMONY VALLEY, 23RD FILING, CITY OF CHEYENNE, LARAMIE COUNTY, WYOMING (LOCATED SOUTH OF WEST ALLISON ROAD, WEST OF WALTERSCHEID BOULEVARD AND NORTH OF WEST COLLEGE DRIVE)."

WHEREAS, Tru Grit Land Development, LLC has subdivided certain land located south of W Allison Road, west of Walterscheid Blvd and north of W College Drive in accordance with applicable Wyoming Statutes;

WHEREAS, Tru Grit Land Development, LLC, the owners of the above-described land, has caused a subdivision plat of said land to be prepared, acknowledged, and certified, particularly describing the lots, blocks, easements and rights-of-way contained therein; and

WHEREAS, the above-described subdivision plat has been presented to the City of Cheyenne Planning Commission for consideration, the Planning Commission has recommended approval of said plat to the Governing Body, and the plat has been duly executed by the Development Office.

NOW, THEREFORE BE IT RESOLVED BY THE GOVERNING BODY OF THE CITY OF CHEYENNE, WYOMING, that the subdivision described as Harmony Valley, 23rd Filing, Cheyenne, Wyoming, be and the same is hereby approved and confirmed as presented, and that the Mayor and the City Clerk are hereby authorized, empowered, and directed to execute the final plat.

PRESENTED, READ AND ADOPTED THIS _____ DAY OF _____, 2026.

Patrick Collins, Mayor

(SEAL)

ATTEST:

Kylie Soden, City Clerk

Line Table		
LINE	LENGTH	BEARING
L102	20.00'	S00°13'36"W
L107	20.00'	S00°13'36"W
L108	20.00'	N00°13'36"E
L113	20.00'	N00°13'36"E
L114	20.00'	S00°13'36"W
L119	20.00'	S00°13'36"W
L132	20.00'	N00°13'36"E
L137	20.00'	N00°13'36"E
L138	20.00'	S00°13'36"W
L143	20.00'	S00°13'36"W
L144	20.00'	N00°13'36"E
L149	20.00'	S00°13'36"E
L150	20.00'	S00°13'36"W
L155	20.00'	S00°13'36"W
L156	20.00'	N00°13'36"E
L161	20.00'	N00°13'36"E
L167	20.00'	S00°13'36"W
L168	16.53'	N03°53'15"E
L169	16.07'	N03°53'15"E
L171	20.00'	S89°46'24"E
L172	20.00'	S89°46'24"E
L173	20.00'	S89°46'24"E
L174	20.00'	S89°46'24"E
L175	20.00'	S89°46'24"E
L176	20.00'	N89°46'24"W
L177	20.00'	N89°46'24"W
L178	20.00'	S89°46'24"E
L179	20.00'	N89°46'24"W
L180	20.00'	N89°46'24"W
L181	20.00'	S89°46'24"E
L182	20.00'	S89°46'24"E
L183	15.92'	N24°49'44"W
L184	15.92'	S24°49'44"E
L185	16.26'	N24°49'44"W
L187	32.66'	S00°07'00"W
L188	31.77'	N00°19'23"E
L189	32.46'	N00°07'00"E
L190	16.37'	N03°53'15"E

- GENERAL NOTES**
1. BASIS OF AZIMUTH – CITY OF CHEYENNE DATUM REFERENCED FROM CITY CONTROL MONUMENTS "ORCHARD" AND "GREELEY".
 2. THE PLATTED AREA DOES NOT FALL WITHIN A FEMA SPECIAL FLOOD HAZARD AREA AS OF THE RECORDING DATE OF THIS DOCUMENT.
 3. UTILITY EASEMENTS SHOWN ALONG STREETS AND LOT LINES ARE 10' WIDE UNLESS OTHERWISE NOTED.
 4. DISTANCES SHOWN ON PLAT ARE GROUND DISTANCE.
 5. FIRE PROTECTION WILL BE PROVIDED BY CITY OF CHEYENNE FIRE DEPARTMENT.
 6. PUBLIC WATER OR WASTE WATER SYSTEMS TO CONNECT TO EXISTING CHEYENNE WATER AND SEWER SYSTEMS.
 7. PROPERTY CORNERS TO BE A SET 1½" ALUMINUM CAP MARKED "PLS 9834" ON 24" LONG #5 REBAR.
 8. REMAINDER LOT 20, BLOCK 3 AND LOT 2, BLOCK 18 MAY BE SUBDIVIDED IN THE FUTURE.

APPROVALS


APPROVED BY THE CITY OF CHEYENNE PLANNING COMMISSION THIS _____ DAY OF _____, 2026.

DEVELOPMENT DIRECTOR, CITY OF CHEYENNE, WYOMING _____

APPROVED BY THE CITY COUNCIL OF THE CITY OF CHEYENNE, LARAMIE COUNTY, WYOMING, THIS _____ DAY OF _____, 2026.

MAYOR _____

ATTEST: _____
CITY CLERK

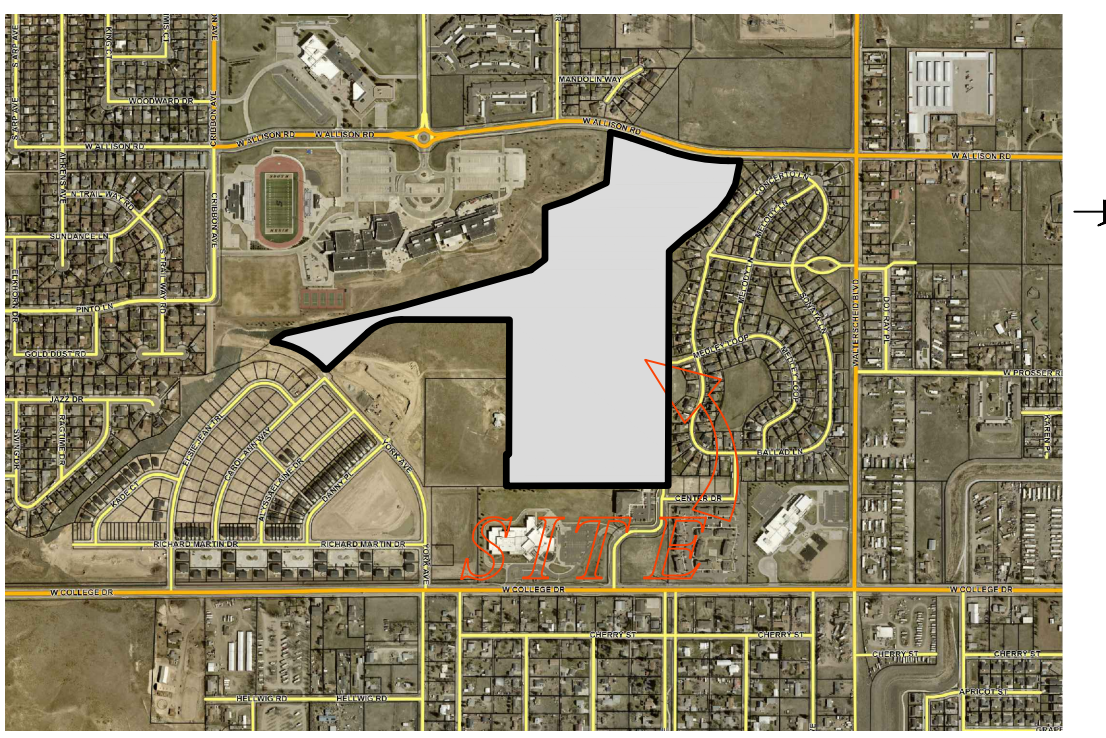


VICINITY MAP NOT TO SCALE

CURVE TABLE						CURVE TABLE						CURVE TABLE					
CURVE #	DELTA	RADIUS	ARC LENGTH	CHORD BEARING	CHORD LENGTH	CURVE #	DELTA	RADIUS	ARC LENGTH	CHORD BEARING	CHORD LENGTH	CURVE #	DELTA	RADIUS	ARC LENGTH	CHORD BEARING	CHORD LENGTH
C105	6° 43' 58"	1105.92'	129.96'	S74° 38' 38"E	129.88'	C141	90° 00' 00"	20.00'	31.42'	N44° 46' 24"W	28.28'	C172	90° 00' 00"	20.00'	31.42'	S45° 13' 36"W	28.28'
C106	18° 04' 45"	1184.06'	373.62'	S80° 22' 44"E	372.07'	C142	90° 00' 00"	20.00'	31.42'	N45° 13' 36"E	28.28'	C173	90° 00' 00"	20.00'	31.42'	N44° 46' 24"W	28.28'
C107	42° 38' 26"	308.00'	229.22'	S68° 54' 23"W	223.97'	C143	90° 00' 00"	20.00'	31.42'	S44° 46' 24"E	28.28'	C174	90° 00' 00"	20.00'	31.42'	N45° 13' 36"E	28.28'
C108	89° 44' 53"	15.00'	23.50'	N87° 33' 50"W	21.17'	C144	90° 00' 00"	20.00'	31.42'	S45° 13' 36"W	28.28'	C175	90° 00' 00"	20.00'	31.42'	S44° 46' 24"E	28.28'
C109	38° 17' 45"	528.00'	352.91'	N61° 50' 16"W	346.38'	C145	90° 00' 00"	20.00'	31.42'	S44° 46' 24"E	28.28'	C177	90° 00' 00"	20.00'	31.42'	S44° 46' 24"E	28.28'
C114	13° 09' 40"	1184.06'	271.98'	S77° 55' 12"E	271.39'	C146	90° 00' 00"	20.00'	31.42'	N44° 46' 24"W	28.28'	C178	90° 00' 00"	20.00'	31.42'	S44° 46' 24"E	28.28'
C115	1° 27' 07"	1184.06'	30.00'	S85° 13' 35"E	30.00'	C147	90° 00' 00"	20.00'	31.42'	N45° 13' 36"E	28.28'	C179	90° 00' 00"	20.00'	31.42'	N45° 13' 36"E	28.28'
C116	1° 27' 06"	1184.06'	30.00'	S86° 40' 42"E	30.00'	C148	90° 00' 00"	20.00'	31.42'	S45° 13' 36"W	28.28'	C180	90° 00' 00"	20.00'	31.42'	S44° 46' 24"E	28.28'
C117	2° 00' 52"	1184.06'	41.63'	S88° 24' 41"E	41.63'	C149	90° 00' 00"	20.00'	31.42'	N44° 46' 24"W	28.28'	C181	90° 00' 00"	20.00'	31.42'	S45° 13' 36"W	28.28'
C119	42° 12' 30"	156.00'	114.92'	N24° 59' 31"E	112.34'	C150	90° 00' 00"	20.00'	31.42'	N45° 13' 36"E	28.28'	C182	90° 00' 00"	20.00'	31.42'	N44° 46' 24"W	28.28'
C120	42° 12' 30"	126.00'	92.82'	N24° 59' 31"E	90.74'	C151	90° 00' 00"	20.00'	31.42'	S44° 46' 24"E	28.28'	C183	90° 00' 00"	20.00'	31.42'	N45° 13' 36"E	28.28'
C121	45° 52' 10"	193.00'	154.51'	N23° 09' 41"E	150.42'	C152	90° 00' 00"	20.00'	31.42'	N45° 13' 36"E	28.28'	C184	90° 00' 00"	20.00'	31.42'	N44° 46' 24"W	28.28'
C122	45° 52' 10"	223.00'	178.53'	N23° 09' 41"E	173.80'	C153	90° 00' 00"	20.00'	31.42'	S44° 46' 24"E	28.28'	C185	90° 00' 00"	20.00'	31.42'	N45° 13' 36"E	28.28'
C123	30° 35' 16"	253.00'	135.07'	N30° 48' 08"E	133.47'	C154	90° 00' 00"	20.00'	31.42'	S45° 13' 36"W	28.28'	C186	90° 00' 00"	20.00'	31.42'	S44° 46' 24"E	28.28'
C124	74° 43' 06"	20.00'	26.08'	N52° 52' 03"E	24.27'	C155	90° 00' 00"	20.00'	31.42'	N44° 46' 24"W	28.28'	C187	90° 00' 00"	20.00'	31.42'	S45° 13' 36"W	28.28'
C125	5° 54' 28"	223.00'	22.99'	N3° 10' 50"E	22.98'	C156	90° 00' 00"	20.00'	31.42'	N45° 13' 36"E	28.28'	C188	90° 00' 00"	20.00'	31.42'	N45° 13' 36"E	28.28'
C126	39° 57' 42"	223.00'	155.53'	N26° 06' 55"E	152.40'	C157	90° 00' 00"	20.00'	31.42'	S44° 46' 24"E	28.28'	C189	90° 00' 00"	20.00'	31.42'	S44° 46' 24"E	28.28'
C127	90° 00' 00"	20.00'	31.42'	S45° 13' 36"W	28.28'	C158	90° 00' 00"	20.00'	31.42'	S45° 13' 36"W	28.28'	C190	90° 00' 00"	20.00'	31.42'	S45° 13' 36"W	28.28'
C128	90° 00' 00"	20.00'	31.42'	N44° 46' 24"W	28.28'	C159	90° 00' 00"	20.00'	31.42'	N44° 46' 24"W	28.28'	C191	90° 00' 00"	20.00'	31.42'	N44° 46' 24"W	28.28'
C129	90° 00' 00"	20.00'	31.42'	N45° 13' 36"E	28.28'	C160	90° 00' 00"	20.00'	31.42'	N45° 13' 36"E	28.28'	C192	90° 00' 00"	20.00'	31.42'	N45° 13' 36"E	28.28'
C130	90° 00' 00"	20.00'	31.42'	S44° 46' 24"E	28.28'	C161	90° 00' 00"	20.00'	31.42'	S44° 46' 24"E	28.28'	C193	90° 00' 00"	20.00'	31.42'	S44° 46' 24"E	28.28'
C131	90° 00' 00"	20.00'	31.42'	S45° 13' 36"W	28.28'	C162	90° 00' 00"	20.00'	31.42'	S45° 13' 36"W	28.28'	C194	25° 03' 20"	95.00'	41.54'	S12° 18' 04"E	41.21'
C132	90° 00' 00"	20.00'	31.42'	N44° 46' 24"W	28.28'	C163	90° 00' 00"	20.00'	31.42'	N44° 46' 24"W	28.28'	C195	25° 03' 20"	65.00'	28.42'	N12° 18' 04"W	28.20'
C133	90° 00' 00"	20.00'	31.42'	N45° 13' 36"E	28.28'	C164	90° 00' 00"	20.00'	31.42'	S45° 13' 36"W	28.28'	C196	25° 03' 20"	35.00'	15.31'	N12° 18' 04"W	15.18'
C134	90° 00' 00"	20.00'	31.42'	S44° 46' 24"E	28.28'	C165	90° 00' 00"	20.00'	31.42'	N44° 46' 24"W	28.28'	C197	24° 56' 44"	165.00'	71.84'	N12° 21' 22"W	71.27'
C135	90° 00' 00"	20.00'	31.42'	N45° 13' 36"E	28.28'	C166	90° 00' 00"	20.00'	31.42'	N45° 13' 36"E	28.28'	C198	25° 09' 07"	135.00'	59.26'	N12° 15' 11"W	58.79'
C136	90° 00' 00"	20.00'	31.42'	N44° 46' 24"W	28.28'	C167	90° 00' 00"	20.00'	31.42'	S44° 46' 24"E	28.28'	C200	90° 00' 00"	20.00'	31.42'	S45° 13' 36"W	28.28'
C137	90° 00' 00"	20.00'	31.42'	N45° 13' 36"E	28.28'	C168	90° 00' 00"	20.00'	31.42'	N45° 13' 36"E	28.28'	C201	24° 56' 44"	105.00'	45.72'	S12° 21' 22"E	45.35'
C138	90° 00' 00"	50.00'	78.54'	N45° 13' 36"E	70.71'	C169	90° 00' 00"	20.00'	31.42'	S44° 46' 24"E	28.28'	C205	42° 12' 30"	186.00'	137.02'	N24° 59' 31"E	133.94'
C139	90° 00' 00"	35.00'	54.98'	N45° 13' 36"E	49.50'	C170	90° 00' 00"	20.00'	31.42'	S45° 13' 36"W	28.28'	C206	90° 00' 00"	20.00'	31.42'	N45° 13' 36"E	28.28'
C140	90° 00' 00"	20.00'	31.42'	S45° 13' 36"W	28.28'	C171	90° 00' 00"	20.00'	31.42'	N44° 46' 24"W	28.28'						

LEGEND

- SET 1-½" ALUMINUM CAP ON 24" LONG #5 REBAR MARKED "PLS 9834"
- FOUND 1-½" ALUMINUM CAP ON 24" LONG #5 REBAR MARKED "PLS 9834"
- FOUND NUMBER 5 REBAR "NO CAP"
- INDICATES EASEMENT LINE

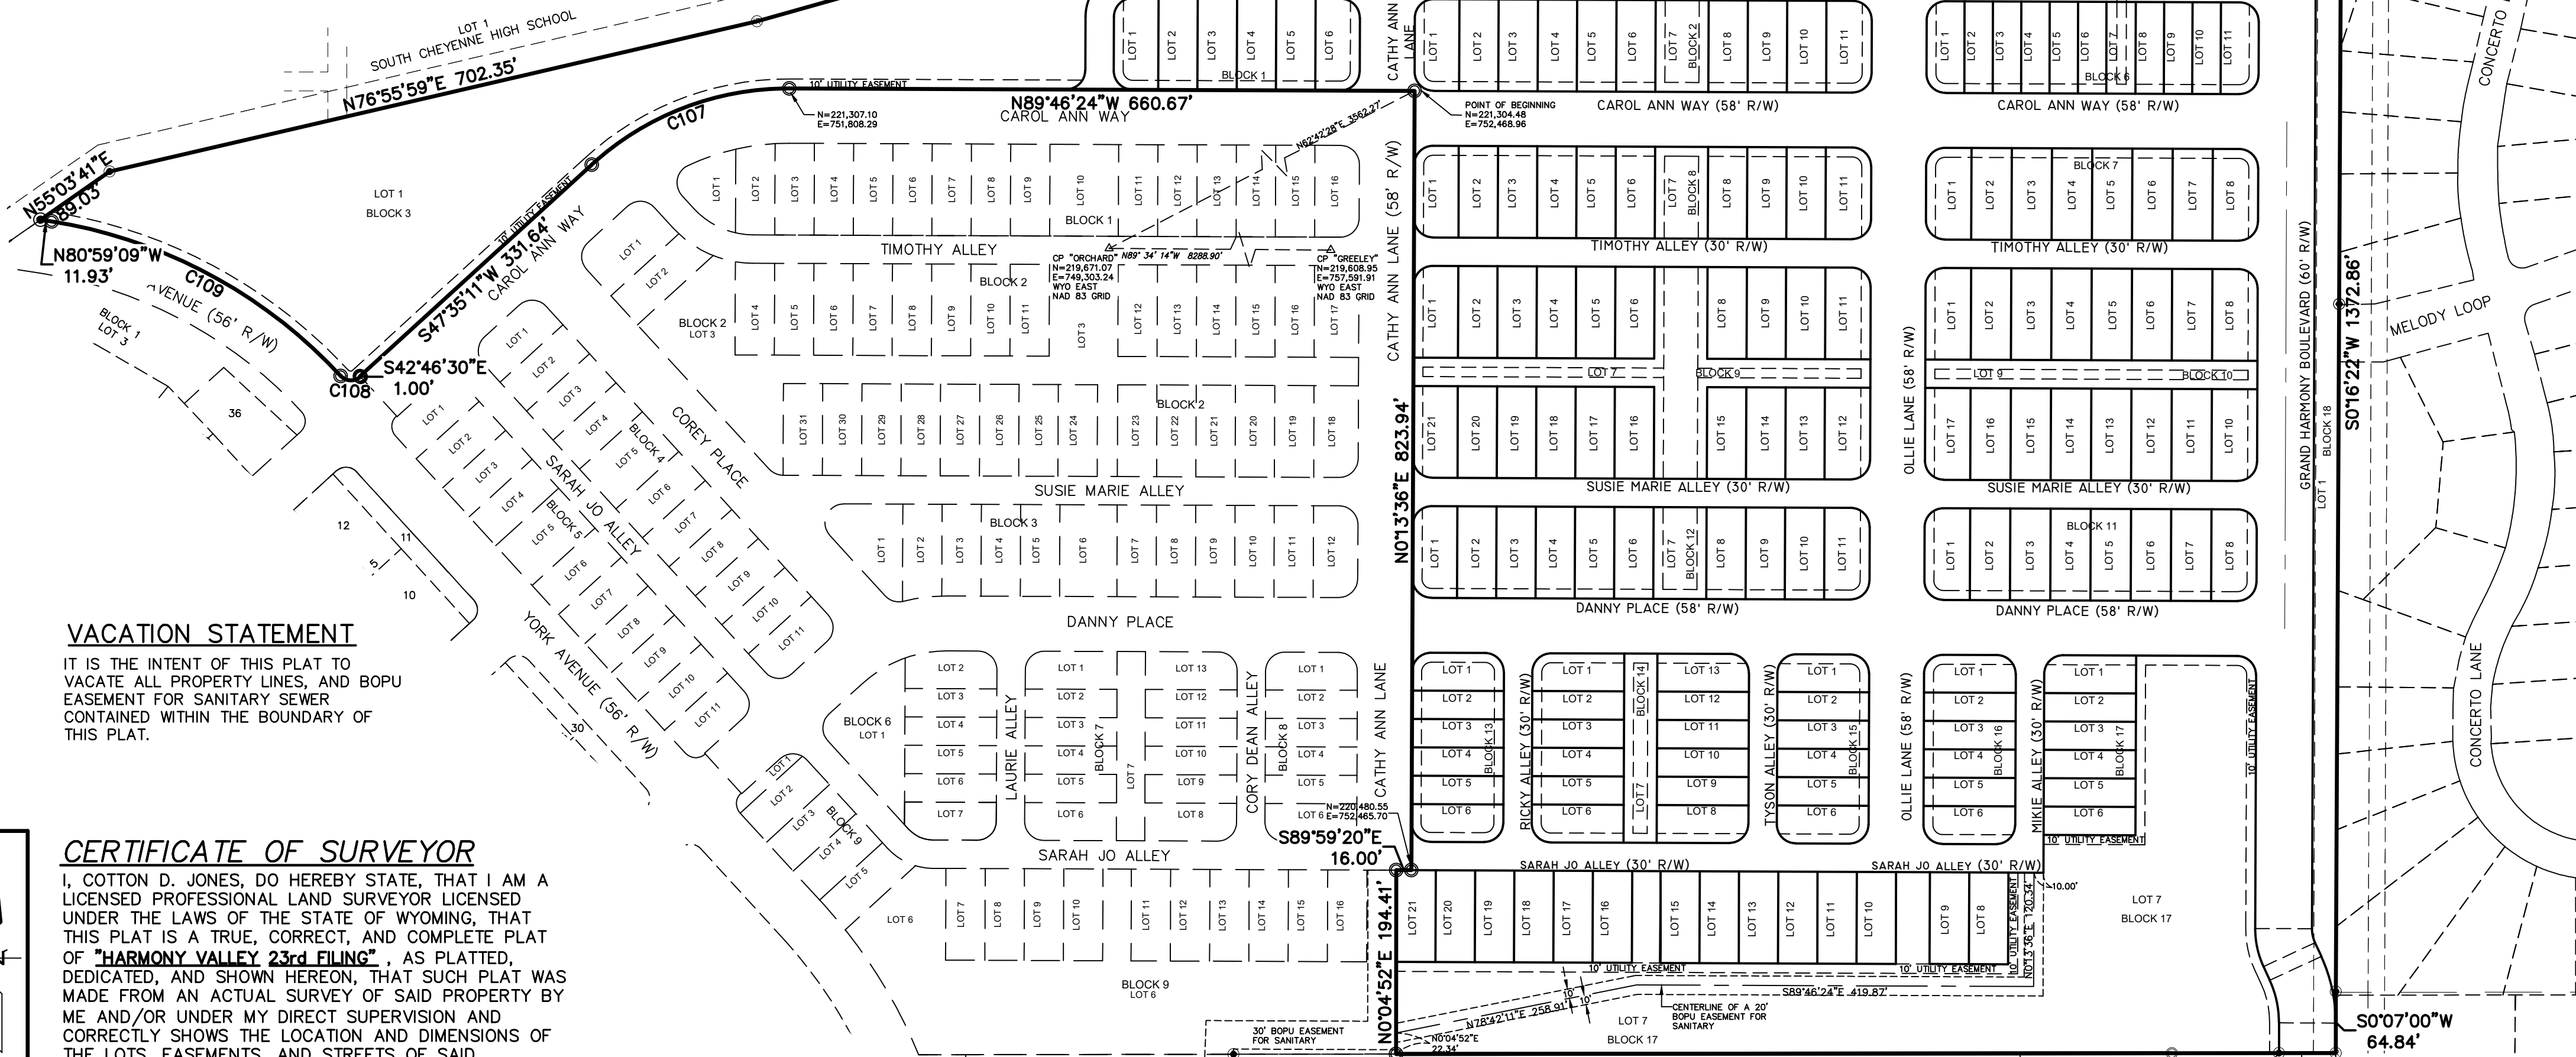

VACATION STATEMENT

IT IS THE INTENT OF THIS PLAT TO VACATE ALL PROPERTY LINES, AND BOPU EASEMENT FOR SANITARY SEWER CONTAINED WITHIN THE BOUNDARY OF THIS PLAT.

CERTIFICATE OF SURVEYOR

I, COTTON D. JONES, DO HEREBY STATE, THAT I AM A LICENSED PROFESSIONAL LAND SURVEYOR LICENSED UNDER THE LAWS OF THE STATE OF WYOMING, THAT THIS PLAT IS A TRUE, CORRECT, AND COMPLETE PLAT OF "HARMONY VALLEY 23rd FILING", AS PLATTED, DEDICATED, AND SHOWN HEREON, THAT SUCH PLAT WAS MADE FROM AN ACTUAL SURVEY OF SAID PROPERTY BY ME AND/OR UNDER MY DIRECT SUPERVISION AND CORRECTLY SHOWS THE LOCATION AND DIMENSIONS OF THE LOTS, EASEMENTS, AND STREETS OF SAID SUBDIVISION AS THE SAME ARE STAKED UPON THE GROUND IN COMPLIANCE WITH THE CITY OF CHEYENNE REGULATIONS GOVERNING THE SUBDIVISION OF LAND.

FILING RECORD

COMMON OPEN SPACE LOTS

OWNERSHIP OF COMMON OPEN SPACE IS PAID BY ALL RESIDENTS WITHIN THE HOA FOR HARMONY VALLEY ESTATES AND ALL MAINTENANCE RESPONSIBILITIES.

COMMON OPEN SPACE LOTS

- LOT 7, BLOCK 2
- LOT 1, BLOCK 3
- LOT 7, BLOCK 4
- LOT 7, BLOCK 5
- LOT 7, BLOCK 6
- LOT 7, BLOCK 8
- LOT 7, BLOCK 9
- LOT 7, BLOCK 10
- LOT 7, BLOCK 12
- LOT 7, BLOCK 17
- LOT 1, BLOCK 18

DEDICATION

KNOW ALL PERSONS BY THESE PRESENTS THAT: TRU-GRIT LAND DEVELOPMENT LLC, A WYOMING LIMITED LIABILITY COMPANY OWNERS IN FEE SIMPLE OF ALL OF LOTS 1-2, BLOCK 10, HARMONY VALLEY 5th FILING AND ALL OF LOT 2, BLOCK 10, HARMONY VALLEY, CITY OF CHEYENNE, LARAMIE COUNTY, WYOMING:

SAID PARCEL CONTAINS 2,159,030 SQ.FT. OR 49.56 ACRES MORE OR LESS.

HAS CAUSED THE SAME TO BE SURVEYED, VACATED, RE-PLATTED AND KNOWN AS HARMONY VALLEY 5th FILING, AND DO HEREBY DECLARE THE SUBDIVISION OF SAID LAND AS IT APPEARS ON THIS RE-PLAT, TO BE THEIR FREE ACT AND DEED AND IN ACCORDANCE WITH THEIR DESIRES AND DO HEREBY DEDICATE FOR THE USE OF THE PUBLIC THE STREETS AND GRANT THE EASEMENTS FOR THE PURPOSES INDICATED HEREON.

TRU-GRIT LAND DEVELOPMENT LLC,
A WYOMING LIMITED LIABILITY COMPANY

EDWARD J. ERNSTE, MANAGER

DEDICATION ACKNOWLEDGEMENTS

STATE OF WYOMING)
COUNTY OF LARAMIE)

THE DEDICATION INSTRUMENT WAS ACKNOWLEDGED BEFORE ME THIS _____ DAY OF _____, 2026,
EDWARD J. ERNSTE, MANAGER OF TRU-GRIT LAND DEVELOPMENT LLC., A WYOMING LIMITED LIABILITY COMPANY.

NOTARY PUBLIC, LARAMIE COUNTY, WYOMING

MY COMMISSION EXPIRES _____

**FINAL PLAT
FOR
HARMONY VALLEY
23rd FILING**


A REPLAT OF ALL OF LOTS 1-2, BLOCK 10, HARMONY VALLEY 5th FILING AND ALL OF LOT 2, BLOCK 10, HARMONY VALLEY 1ST FILING
CITY OF CHEYENNE, LARAMIE COUNTY, WYOMING

PREPARED: 3/5/26 SHEET 1 OF 2 REVISED:

Licensed in:
WY, CO, MT, SD,
ND, ID, UT, NV

6750 Say Kally Rd.,
Cheyenne, WY 82009
Ph: 307-637-7107
Cell: 307-630-8550
Email: cotton.jones@msn.com


CURVE TABLE						CURVE TABLE						CURVE TABLE					
CURVE #	DELTA	RADIUS	ARC LENGTH	CHORD BEARING	CHORD LENGTH	CURVE #	DELTA	RADIUS	ARC LENGTH	CHORD BEARING	CHORD LENGTH	CURVE #	DELTA	RADIUS	ARC LENGTH	CHORD BEARING	CHORD LENGTH
C105	6° 43' 58"	1105.92'	129.96'	S74° 38' 39"E	129.88'	C141	90° 00' 00"	20.00'	31.42'	N44° 46' 24"W	28.28'	C172	90° 00' 00"	20.00'	31.42'	S45° 13' 36"W	28.28'
C106	18° 04' 45"	1184.06'	373.62'	S80° 22' 44"E	372.07'	C142	90° 00' 00"	20.00'	31.42'	N45° 13' 36"E	28.28'	C173	90° 00' 00"	20.00'	31.42'	N44° 46' 24"W	28.28'
C107	42° 38' 26"	308.00'	229.22'	S68° 54' 23"W	223.97'	C143	90° 00' 00"	20.00'	31.42'	S44° 46' 24"E	28.28'	C174	90° 00' 00"	20.00'	31.42'	N45° 13' 36"E	28.28'
C108	89° 44' 53"	15.00'	23.50'	N87° 33' 50"W	21.17'	C144	90° 00' 00"	20.00'	31.42'	S45° 13' 36"W	28.28'	C175	90° 00' 00"	20.00'	31.42'	S44° 46' 24"E	28.28'
C109	38° 17' 45"	528.00'	352.91'	N61° 50' 16"W	346.38'	C145	90° 00' 00"	20.00'	31.42'	S44° 46' 24"E	28.28'	C176	90° 00' 00"	20.00'	31.42'	N45° 13' 36"E	28.28'
C114	13° 09' 40"	1184.06'	271.98'	S77° 55' 12"E	271.39'	C146	90° 00' 00"	20.00'	31.42'	N44° 46' 24"W	28.28'	C178	90° 00' 00"	20.00'	31.42'	S44° 46' 24"E	28.28'
C115	1° 27' 07"	1184.06'	30.00'	S85° 13' 35"E	30.00'	C147	90° 00' 00"	20.00'	31.42'	N45° 13' 36"E	28.28'	C179	90° 00' 00"	20.00'	31.42'	N45° 13' 36"E	28.28'
C116	1° 27' 06"	1184.06'	30.00'	S86° 40' 42"E	30.00'	C148	90° 00' 00"	20.00'	31.42'	S45° 13' 36"W	28.28'	C180	90° 00' 00"	20.00'	31.42'	S44° 46' 24"E	28.28'
C117	2° 00' 52"	1184.06'	41.63'	S88° 24' 41"E	41.63'	C149	90° 00' 00"	20.00'	31.42'	N44° 46' 24"W	28.28'	C181	90° 00' 00"	20.00'	31.42'	S45° 13' 36"W	28.28'
C119	42° 12' 30"	156.00'	114.92'	N24° 59' 31"E	112.34'	C150	90° 00' 00"	20.00'	31.42'	N45° 13' 36"E	28.28'	C182	90° 00' 00"	20.00'	31.42'	N44° 46' 24"W	28.28'
C120	42° 12' 30"	126.00'	92.82'	N24° 59' 31"E	90.74'	C151	90° 00' 00"	20.00'	31.42'	S44° 46' 24"E	28.28'	C183	90° 00' 00"	20.00'	31.42'	N45° 13' 36"E	28.28'
C121	45° 52' 10"	193.00'	154.51'	N23° 09' 41"E	150.42'	C152	90° 00' 00"	20.00'	31.42'	N45° 13' 36"E	28.28'	C184	90° 00' 00"	20.00'	31.42'	N44° 46' 24"W	28.28'
C122	45° 52' 10"	223.00'	178.53'	N23° 09' 41"E	173.80'	C153	90° 00' 00"	20.00'	31.42'	S44° 46' 24"E	28.28'	C185	90° 00' 00"	20.00'	31.42'	N45° 13' 36"E	28.28'
C123	30° 35' 16"	253.00'	135.07'	N30° 48' 08"E	133.47'	C154	90° 00' 00"	20.00'	31.42'	S45° 13' 36"W	28.28'	C186	90° 00' 00"	20.00'	31.42'	S44° 46' 24"E	28.28'
C124	74° 43' 06"	20.00'	26.08'	N52° 52' 03"E	24.27'	C155	90° 00' 00"	20.00'	31.42'	N44° 46' 24"W	28.28'	C187	90° 00' 00"	20.00'	31.42'	S45° 13' 36"W	28.28'
C125	5° 54' 28"	223.00'	22.99'	N3° 10' 50"E	22.98'	C156	90° 00' 00"	20.00'	31.42'	N45° 13' 36"E	28.28'	C188	90° 00' 00"	20.00'	31.42'	N45° 13' 36"E	28.28'
C126	39° 57' 42"	223.00'	155.53'	N26° 06' 55"E	152.40'	C157	90° 00' 00"	20.00'	31.42'	S44° 46' 24"E	28.28'	C189	90° 00' 00"	20.00'	31.42'	S44° 46' 24"E	28.28'
C127	90° 00' 00"	20.00'	31.42'	S45° 13' 36"W	28.28'	C158	90° 00' 00"	20.00'	31.42'	S45° 13' 36"W	28.28'	C190	90° 00' 00"	20.00'	31.42'	S45° 13' 36"W	28.28'
C128	90° 00' 00"	20.00'	31.42'	N44° 46' 24"W	28.28'	C159	90° 00' 00"	20.00'	31.42'	N44° 46' 24"W	28.28'	C191	90° 00' 00"	20.00'	31.42'	N44° 46' 24"W	28.28'
C129	90° 00' 00"	20.00'	31.42'	N45° 13' 36"E	28.28'	C160	90° 00' 00"	20.00'	31.42'	N45° 13' 36"E	28.28'	C192	90° 00' 00"	20.00'	31.42'	N45° 13' 36"E	28.28'
C130	90° 00' 00"	20.00'	31.42'	S44° 46' 24"E	28.28'	C161	90° 00' 00"	20.00'	31.42'	S44° 46' 24"E	28.28'	C193	90° 00' 00"	20.00'	31.42'	S44° 46' 24"E	28.28'
C131	90° 00' 00"	20.00'	31.42'	S45° 13' 36"W	28.28'	C162	90° 00' 00"	20.00'	31.42'	S45° 13' 36"W	28.28'	C194	25° 03' 20"	95.00'	41.54'	S12° 18' 04"E	41.21'
C132	90° 00' 00"	20.00'	31.42'	N44° 46' 24"W	28.28'	C163	90° 00' 00"	20.00'	31.42'	N44° 46' 24"W	28.28'	C195	25° 03' 20"	65.00'	28.42'	N12° 18' 04"W	28.20'
C133	90° 00' 00"	20.00'	31.42'	S45° 13' 36"E	28.28'	C164	90° 00' 00"	20.00'	31.42'	S45° 13' 36"E	28.28'	C196	25° 03' 20"	35.00'	15.31'	N12° 18' 04"W	15.18'
C134	90° 00' 00"	20.00'	31.42'	S44° 46' 24"E	28.28'	C165	90° 00' 00"	20.00'	31.42'	N44° 46' 24"W	28.28'	C197	24° 56' 44"	165.00'	71.84'	N12° 21' 22"W	71.27'
C135	90° 00' 00"	20.00'	31.42'	N45° 13' 36"E	28.28'	C166	90° 00' 00"	20.00'	31.42'	N45° 13' 36"E	28.28'	C198	25° 09' 07"	135.00'	59.26'	N12° 15' 11"W	58.79'
C136	90° 00' 00"	20.00'	31.42'	N44° 46' 24"W	28.28'	C167	90° 00' 00"	20.00'	31.42'	S44° 46' 24"E	28.28'	C200	90° 00' 00"	20.00'	31.42'	S45° 13' 36"W	28.28'
C137	90° 00' 00"	20.00'	31.42'	N45° 13' 36"E	28.28'	C168	90° 00' 00"	20.00'	31.42'	N45° 13' 36"E	28.28'	C201	24° 56' 44"	105.00'	45.72'	S12° 21' 22"E	45.35'
C138	90° 00' 00"	50.00'	78.54'	N45° 13' 36"E	70.71'	C169	90° 00' 00"	20.00'	31.42'	S44° 46' 24"E	28.28'	C205	42° 12' 30"	186.00'	137.02'	N24° 59' 31"E	133.94'
C139	90° 00' 00"	35.00'	54.98'	N45° 13' 36"E	49.50'	C170	90° 00' 00"	20.00'	31.42'	S45° 13' 36"E	28.28'	C206	90° 00' 00"	20.00'	31.42'	N45° 13' 36"E	28.28'
C140	90° 00' 00"	20.00'	31.42'	S45° 13' 36"W	28.28'	C171	90° 00' 00"	20.00'	31.42'	N44° 46' 24"W	28.28'						

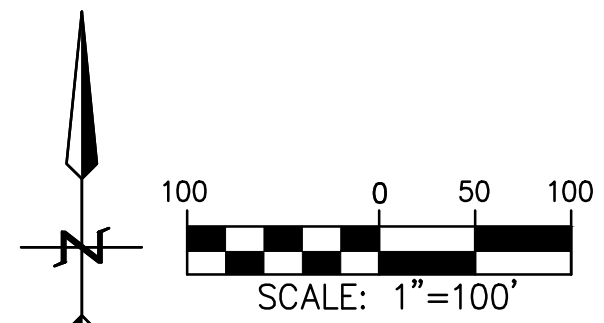

VACATION STATEMENT

IT IS THE INTENT OF THIS PLAT TO VACATE ALL PROPERTY LINES, AND BOPU EASEMENT FOR SANITARY SEWER CONTAINED WITHIN THE BOUNDARY OF THIS PLAT.

FILING RECORD

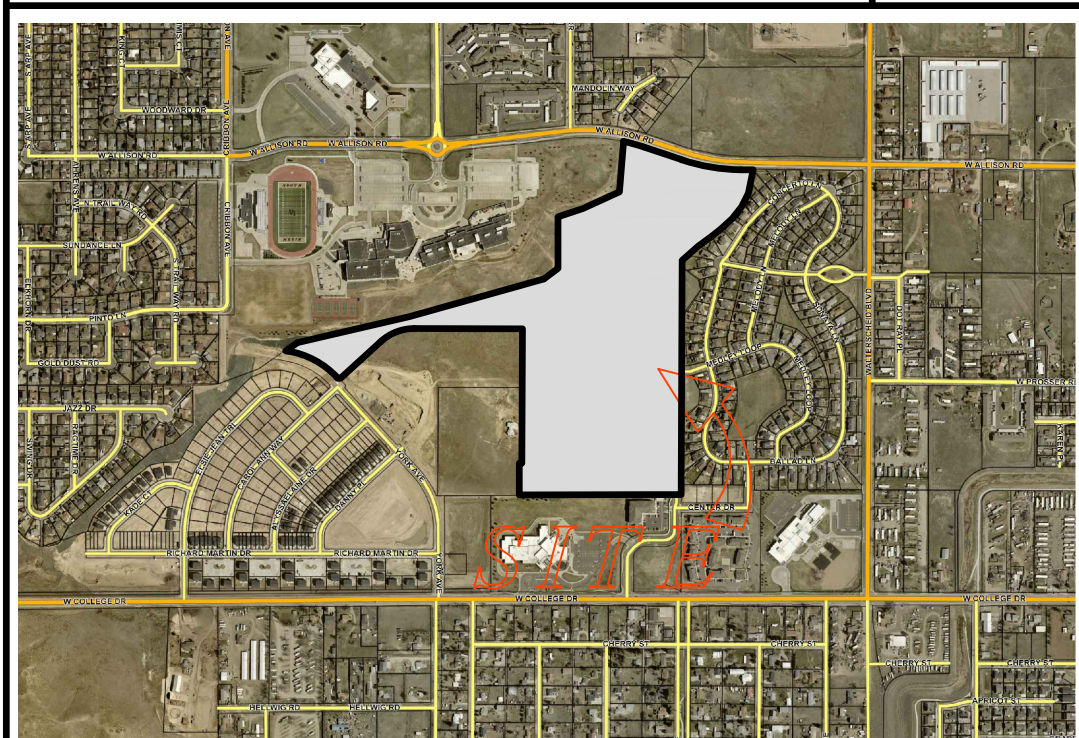

VICINITY MAP

NOT TO SCALE

COMMON OPEN SPACE LOTS

OWNERSHIP OF COMMON OPEN SPACE IS PAID BY ALL RESIDENTS WITHIN THE HOA FOR HARMONY VALLEY ESTATES AND ALL MAINTENANCE RESPONSIBILITIES.

Line Table

LINE	LENGTH	BEARING
L102	20.00'	S00°13'36"W
L107	20.00'	S00°13'36"W
L108	20.00'	N00°13'36"E
L113	20.00'	N00°13'36"E
L114	20.00'	S00°13'36"W
L119	20.00'	S00°13'36"W
L132	20.00'	N00°13'36"E
L137	20.00'	N00°13'36"E
L138	20.00'	S00°13'36"W
L143	20.00'	S00°13'36"W
L144	20.00'	N00°13'36"E
L149	20.00'	N00°13'36"E
L150	20.00'	S00°13'36"W
L155	20.00'	S00°13'36"W
L156	20.00'	N00°13'36"E
L161	20.00'	S00°13'36"W
L167	20.00'	S00°13'36"W
L168	16.53'	N03°53'15"E
L169	16.07'	N03°53'15"E
L171	20.00'	S89°46'24"E
L172	20.00'	S89°46'24"E
L173	20.00'	S89°46'24"E
L174	20.00'	S89°46'24"E
L175	20.00'	S89°46'24"E
L176	20.00'	N89°46'24"W
L177	20.00'	N89°46'24"W
L178	20.00'	S89°46'24"E
L179	20.00'	N89°46'24"W
L180	20.00'	N89°46'24"W
L181	20.00'	S89°46'24"E
L182	20.00'	S89°46'24"E
L183	15.92'	N24°49'44"W
L184	15.92'	S24°49'44"E
L185	16.26'	N24°49'44"W
L187	32.66'	S00°07'00"W
L188	31.77'	N00°19'23"E
L189	32.46'	N00°07'00"E
L190	16.37'	N03°53'15"E

COMMON OPEN SPACE LOTS

LOT 7, BLOCK 2
LOT 1, BLOCK 3
LOT 7, BLOCK 4
LOT 7, BLOCK 5
LOT 7, BLOCK 6
LOT 7, BLOCK 8
LOT 9, BLOCK 10
LOT 7, BLOCK 12
LOT 7, BLOCK 14
LOT 7, BLOCK 17
LOT 1, BLOCK 18

LEGEND

- SET 1-1/2" ALUMINUM CAP ON 24" LONG #5 REBAR MARKED "PLS 9834"
- FOUND 1-1/2" ALUMINUM CAP ON 24" LONG #5 REBAR MARKED "PLS 9834"
- ⊗ FOUND NUMBER 5 REBAR "NO CAP"
- INDICATES EASEMENT LINE

GENERAL NOTES

- BASIS OF AZIMUTH – CITY OF CHEYENNE DATUM REFERENCED FROM CITY CONTROL MONUMENTS "ORCHARD" AND "GREELEY".
- THE PLATTED AREA DOES NOT FALL WITHIN A FEMA SPECIAL FLOOD HAZARD AREA AS OF THE RECORDING DATE OF THIS DOCUMENT.
- UTILITY EASEMENTS SHOWN ALONG STREETS AND LOT LINES ARE 10' WIDE UNLESS OTHERWISE NOTED.
- DISTANCES SHOWN ON PLAT ARE GROUND DISTANCE.
- FIRE PROTECTION WILL BE PROVIDED BY CITY OF CHEYENNE FIRE DEPARTMENT.
- PUBLIC WATER OR WASTE WATER SYSTEMS TO CONNECT TO EXISTING CHEYENNE WATER AND SEWER SYSTEMS.
- PROPERTY CORNERS TO BE A SET 1 1/2" ALUMINUM CAP MARKED "PLS 9834" ON 24" LONG #5 REBAR.
- REMAINDER LOT 20, BLOCK 3 AND LOT 2, BLOCK 18 WILL BE SUBDIVIDED IN THE FUTURE.

FINAL PLAT FOR HARMONY VALLEY 23rd FILING

A REPLAT OF ALL OF LOTS 1–2, BLOCK 10,
HARMONY VALLEY 5TH FILING
AND ALL OF LOT 2, BLOCK 10,
HARMONY VALLEY 1ST FILING
CITY OF CHEYENNE, LARAMIE COUNTY, WYOMING

PREPARED: 3/5/26

SHEET 2 OF 2

REVISED:



CITY OF
CHEYENNE
— PLANNING & DEVELOPMENT —

CITY OF CHEYENNE PLANNING COMMISSION
MAY 4, 2026
STAFF REPORT

FILE: PUDC-26-50: Harmony Valley, 23rd Filing (Expedited Review)

REQUEST: Subdivision of a three large Lots into 196 Lots.

LOCATION: South of W Allison Road, North of W College Drive.

APPLICANT: John Sayers

OWNER: Tru Grit Land Development LLC

ZONING: NR-3 Neighborhood Residential High-density

PURPOSE: A plat creating 196 Lots for residential development.

PREPARED BY: Connor White, Planner II



RECOMMENDED MOTION:

Move to **approve** the Harmony Valley, 23rd Filing Preliminary Plat, advancing the Final Plat to the Governing Body with staff recommended conditions.

APPLICABLE CITY CODE SECTION(S) AND PLANS:

- UDC 2.1.2 Preliminary Plat Approval
- UDC 2.1.3 Final Plat Approval
- UDC Article 4 Subdivisions
- UDC Article 5 Zoning Regulations
- PlanCheyenne

BACKGROUND:

The applicant is requesting approval of an expedited plat for roughly 49.56 acres of land. The proposed plat would create 196 Lots, 184 for single-family residential development and 12 open space lots. The proposed development similar to that of Harmony Valley 5th, Filing to the west and will be developed using the Cottage Lot section of the UDC.

SURROUNDING LAND USE AND ZONING:

	Future Land Use Designation	Zoning	Land Use
Subject Site	Urban Residential / Mixed-use Residential	NR-3 Neighborhood Residential – High-density	Vacant
North	Urban Residential / Public / Mixed-use Commercial	P – Public, MR-Medium-density Residential and NR-3	School, single-family and vacant land
South	Public / Mixed-use Commercial	MUB – Mixed-use Business	School and Multifamily
East	Urban Residential	PUD – Planned Unit Development	Single-family
West	Urban Residential / Mixed-use Residential	NR-3 and PUD	Vacant and single-family

ANALYSIS OF APPLICATION CONFORMANCE WITH REVIEW CRITERIA:

Should the Planning Commission wish to recommend approval of the Expedited Preliminary Plat, the Commission must make the following findings required in UDC 2.1.2.d and 2.1.3.d – a detailed analysis of which is below:

1) The application is in accordance with the development policies and physical patterns identified in the Comprehensive Plan. (UDC 2.1.2.d.1)

On the future land use map found in PlanCheyenne, the subject land has been designated as Urban Residential and Mixed-use Residential. The Urban Residential designation encourages a range of residential uses. The Mixed-use Residential designation would encourage denser residential development with a mix of commercial uses. The proposed plat is to provide additional single-family residential to the area at a higher density by using the Cottage Lot section of the UDC and creating smaller lots.

Foundation 1 of PlanCheyenne encourages community growth. This development is in response to market demands and is within the Urban Service Boundary. The development patterns proposed by this plat are compatible with the designations found on the future land use map.

The application **complies** with this review criterion.

2) The application reflects sound planning and urban design principles with respect to existing and potential future development in the vicinity, including consideration of current and future streets, open spaces, blocks and lots, and public utilities or facilities. (UDC 2.1.2.d.2)

The proposed plat subdivides three larger parcels into 184 residential lots that meet the standards of UDC 6.6.5 Cottage Lots. This plat adds additional roads, alleys and extends the utilities in the area allowing for further development. The development pattern matches the recently approved development to the west continuing the same development pattern and lot sizes. This plat also provides buffers to neighboring developments via open space common lots. There is a possible connection to the subdivision to the east via Medley Loop, but due to the original grading of the area to the east and the WAPA lines, a street connection is not logical at this time. A pedestrian connection appears possible but may require additional engineering. Should the connection be possible, an easement will need to be provided.

The application **complies** with this review criterion, with conditions.

3) The division of land meets the purposes, intent, and all applicable standards in Article 4. (UDC 2.1.2.d.3)

Community Facility Fees (4.2):

For fees based on acreage, the area of the plat is pro-rated to the nearest tenth of an acre. Lands reserved as unbuildable (for right-of-way, detention, parks, remainder lots, etc), are exempt from fees. Park fees are calculated at \$700 per acre. All fees are due at the time of building permit.

Per UDC Section 4.2.5, Table 4-2, Enhancement Fees are payable at the issuance of a building permit for each structure. The Residential Enhancement Fee is \$400 per dwelling unit

Transportation Network (4.3):

This plat is creating additional streets and alleys that will add to the street network in the area and provide access to the new subdivision. The blocks around the perimeter of the proposed

subdivision do not meet block size requirements. Lot 1, Block 18 has a potential connection via dedicated right-of-way, but due to the original grading of the area to the east and the WAPA lines, a street connection is not logical at this time. A pedestrian connection appears possible and the applicant would like to finalize engineering prior to putting on a pedestrian easement. The other large blocks in the area have topographic constraints and public facilities that would not allow for additional connections. Staff recommends an exception to block size.

Open Space (4.4):

The plat proposes 12 open space lots throughout the subdivision. Additional open space lots were also provided with 5th filing and a park was provided with 1st filing.

Required Improvements (4.5):

This plat appears to be able to provide all required utilities to the lots within this development.

Public Safety Fees (4.6):

Public Safety Fees are required at the time of construction of any residential building on any of the proposed lots. Per UDC Section 4.6.3.b, Public Safety Fees are payable at the issuance of a building permit for each structure.

The application **complies** with this review criterion, with conditions.

- 4) Any phasing proposed in the application is clearly indicated and demonstrates a logical and well-planned development pattern. This may include consideration of amenities and public facilities of the subdivision within each phase compared to the anticipated timing or the likelihood of future phases being constructed as planned. (UDC 2.1.2.d.4)**

No specific phasing is proposed with this project.

Review criterion **not applicable**.

- 5) The impacts identified in specific studies or technical reports that were prepared or requested to be prepared in association with the application, and whether the findings and recommendations of these reports, or any modifications or conditions on approval of the application, can mitigate these impacts. (UDC 2.1.2.d.5)**

Drainage:

A drainage study was submitted and reviewed. There were no concerns with drainage at the plat level for the project as presented.

Traffic:

A transportation study was submitted and reviewed with Harmony Valley 5th Filing which took this subdivision into account. A Traffic Impact Letter was submitted with this plat detailing how the proposed plat still met the findings of the study. There were no concerns with traffic at the plat level for the project as presented.

The application **complies** with this review criterion.

- 6) Lots proposed for development shall be buildable lots according to the existing or proposed zoning district standards, result in design and development patterns that meet the Intent and Applicability statements of the existing or proposed zoning district, and not aggravate nonconforming setbacks or currently adopted building and fire code access and separation requirements. (UDC 2.1.2.d.6)**

All lots proposed for development are buildable lots in this zone district.

The application **complies** with this review criterion.

- 7) All parcels not proposed as buildable lots and which are not dedicated to and accepted by the City shall have a clearly defined entity responsible for ongoing maintenance. (UDC 2.1.2.d.7)**

The Plat designates multiple lots as unbuildable. Lot 20, Block 3 and Lot 2, Block 18 are designated as remainder lots. These lots will need to be replatted in the future should that lot wish to be developed or sold. Multiple other lots are common lots which are proposed to be under common ownership and maintained by a Home Owners Association. Common open space lots are an expected part of cottage lot development.

The application **complies** with this review criterion.

- 8) The application will not create any undue influence on existing or potential development for adjacent property considering the existing zoning and Comprehensive Plan policies for that property. (UDC 2.1.2.d.8)**

This plat will not create any undue influence on existing or potential development. This plat creates a street network that ties into the subdivision to the west, W Allison to the north and Grand Harmony Blvd to the south. The land to the east is already developed with single-family homes. Due to the step grade of Medley Loop a vehicular connection can not be made, but there may be potential for a pedestrian connection linking the two subdivisions.

The application **complies** with this review criterion.

- 9) The application is not harmful to the public health, safety, and welfare. (UDC 2.1.2.d.9)**

City staff is satisfied that this proposed plat would not adversely affect the public health, safety, or general welfare.

The application **complies** with this review criterion.

- 10) Remainder lot(s) shall be clearly identified on the preliminary plat and shall not be developed or proposed for development for purposes. Remainder lot(s) shall be noted and described on all plats either graphically or by legal description. (UDC 2.1.2.d.10)**

Lot 20, Block 3 and Lot 2, Block 18 are designated as remainder lots. Note 8 clearly labels them as such.

The application **complies** with this review criterion.

11) The layout and design of the final plat is in substantial compliance with the approved preliminary plat considering the number of lots or parcels, street and block layout, and access, and any deviations in the final plat brings the application in further compliance with the Comprehensive Plan. (UDC 2.1.3.d.1)

The Final Plat submitted with the application is substantially similar to the Preliminary Plat submitted.

The application **complies** with this review criterion.

12) The application meets any conditions or modifications of the approved preliminary plat. (UDC 2.1.3.d.2)

Through staff's review the a pedestrian access will need to be added to connect Medley Loop to Grand Harmony Blvd. At this time the applicant is working on how that connection will work and does not know exactly where the easement will be needed. The easement should be added before signing of the plat or by separate instrument once the engineering for the connection is completed.

The application **complies** with this review criterion, with conditions.

13) The application meets the purposes, intent, and applicable standards of Article 4. (UDC 2.1.3.d.3)

As a concurrent Preliminary and Final Plat application, this Final Plat review criterion is covered by the equivalent Preliminary Plat review criterion (subsection 3 above).

The application **complies** with this review criterion.

CONFORMANCE WITH APPLICABLE PLANS:

The project is located in an area covered by the following plans:

- PlanCheyenne

Conformance with PlanCheyenne is covered by review criterion 1.

PUBLIC NOTICE AND PUBLIC COMMENTS RECEIVED:

Although projects have public notice and the opportunity for public comments, projects are required to be approved or denied based on the review criteria (listed above). Public comments relevant to the review criteria may assist the review and discussion on the application.

The public was given notice of the project in the following ways:

- **Legal Notice** in the Wyoming Tribune Eagle published on April 18, 2026.
- **Posted Notice** Evidence of posted notice was provided showing that the signs were posted on April 24, 2026.
- **Internet Posting** on connect.cheyennecity.org on March 13, 2026.

As of the publication of the Staff Report (April 27, 2026), Staff has received no inquiries or comments from the public on this project. The project page on the website has received 86 views and no comments.

STAFF REVIEW:

Through the review process, comments were received regarding the following issues:

1. Technical correction
2. Easements

CONCLUSION:

Staff analysis is that the application meets the review criteria and therefore recommends approval of the expedited plat application with conditions.

ALTERNATIVES:

1. Recommend approval of the expedited preliminary plat, forwarding the Final Plat to the Governing Body.
2. Recommend approval of the preliminary plat with conditions and that a final plat addressing the conditions of approval be prepared and presented to the Governing Body.
3. Recommend approval of the preliminary plat as submitted by the applicant and forward the preliminary plat to the Governing Body.
4. Recommend approval of the preliminary plat subject to staff's recommended conditions and forward the preliminary plat to the Governing Body.
5. Recommend denial of the preliminary plat based on findings of denial. The Planning Commission must conclude that the project does not meet all the review criteria. As part of the motion, findings for denial must be stated.
6. Postpone the project until issues identified during the meeting can be resolved.

General Information Regarding Alternatives:

The Planning Commission may modify staff's recommended conditions, delete conditions, add conditions, or decide contrary to staff's recommendation. In the event conditions are modified, the conditions shall relate to applicable review criteria. In the event that the Commission acts contrary to staff's recommendation or modifies conditions of approval, the Commission shall cite specific reasons (based on the review criteria) for approval or denial.



STAFF RECOMMENDATION:

Staff recommends approval of the expedited Preliminary Plat, advancing the Final Plat to the Governing Body with the following conditions and exceptions:

1. The following exceptions be granted:
 - a. Exceptions to block size for perimeter blocks due to topography and civic uses.
2. Prior to recording of the final plat:
 - a. A pedestrian access easement be provided connecting Medley Loop to Grand Harmony Blvd. If, after extensive engineering, the City Engineer determines a pedestrian connection is not feasible, the Director may waive or modify this condition.

ATTACHMENTS:

1. Zoning Map
2. Land Use Plan Map
3. Master Application Form
4. Preliminary Plat
5. Final Plat

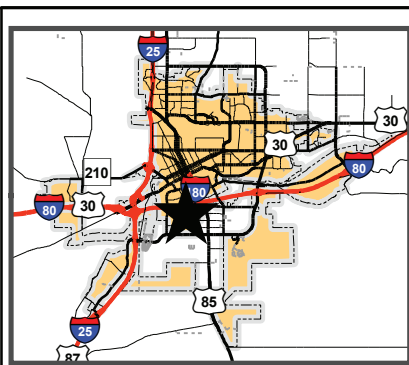
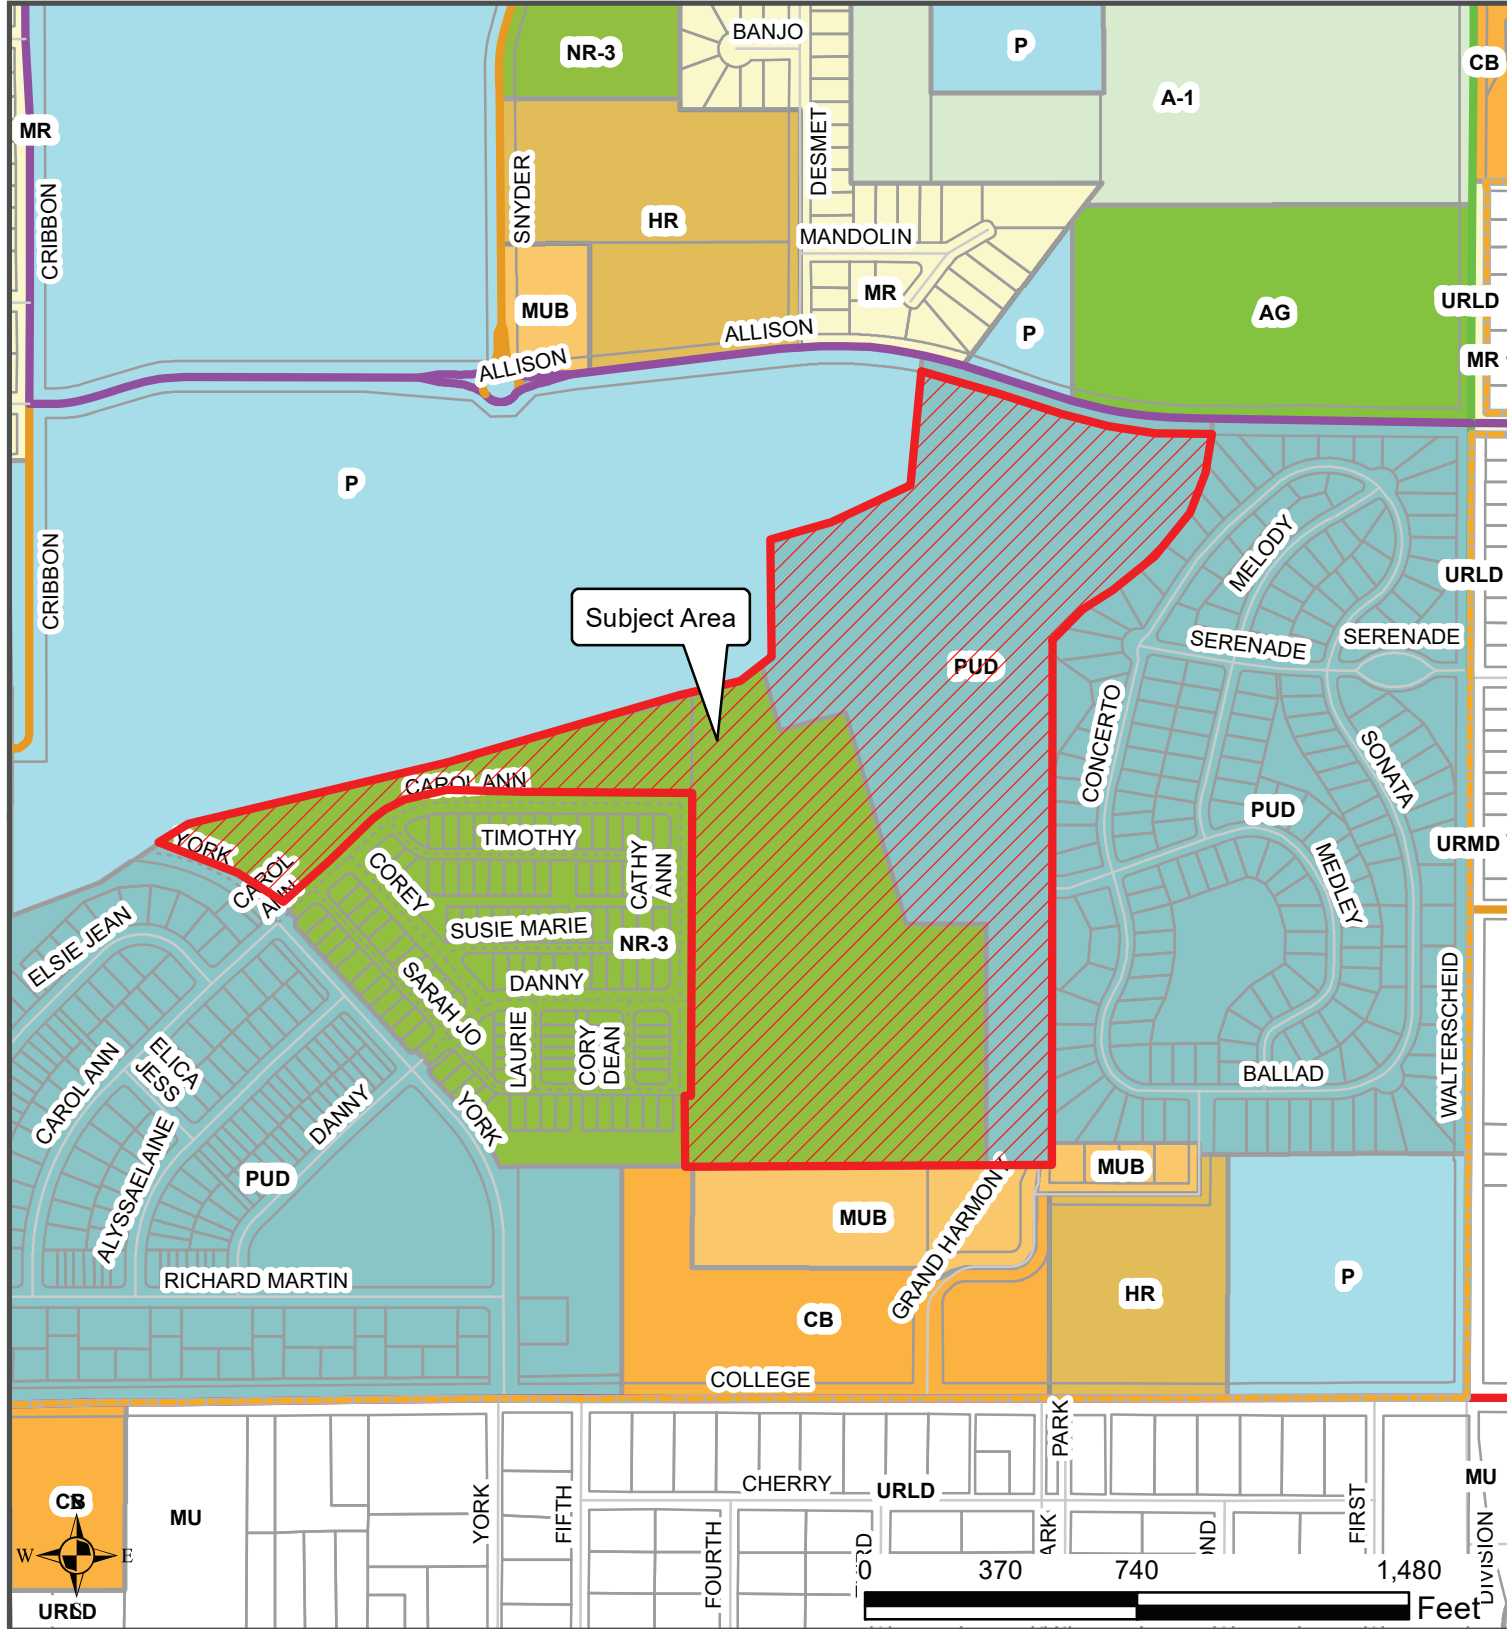


Attachment 1: Zoning Map PUDC-26-50

This map/data is made possible through the Cheyenne and Laramie County Cooperative GIS (CLCCGIS) Program and is for display purposes only. The CLCCGIS invokes its sovereign and governmental immunity in allowing access to or use of this data, makes no warranties as to the validity, and assumes no liability associated with the use or misuse of this information.

Legend

	Nov19_CityLimits		A-1 / Agricultural and Rural Residential
	Interstate		A-2 / Agricultural
	Principal Arterial		AG / City Agricultural
	Minor Arterial		MUR / Mixed Use Residential Emphasis
	Major Collector		CBD / Central Business District
	Minor Collector		CB / Community Business
	Local		NB / Neighborhood Business
	Private		MU / Mixed Use - County
	Platted not built		MUB / Mixed Use Business Emphasis
	HR / High Density Residential		MUE / Mixed Use Employment Emphasis
	MR / Medium Density Residential		HI / Heavy Industrial
	LR / Low Density Residential		LI / Light Industrial
	NR-2 / Neighborhood Residential - Med. Density		P / Public
	NR-3 / Neighborhood Residential - High Density		AD / Airport District
	AR / Agricultural Residential		PUD / Planned Unit Development
			X / Exempt

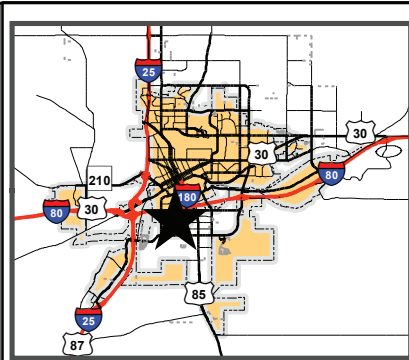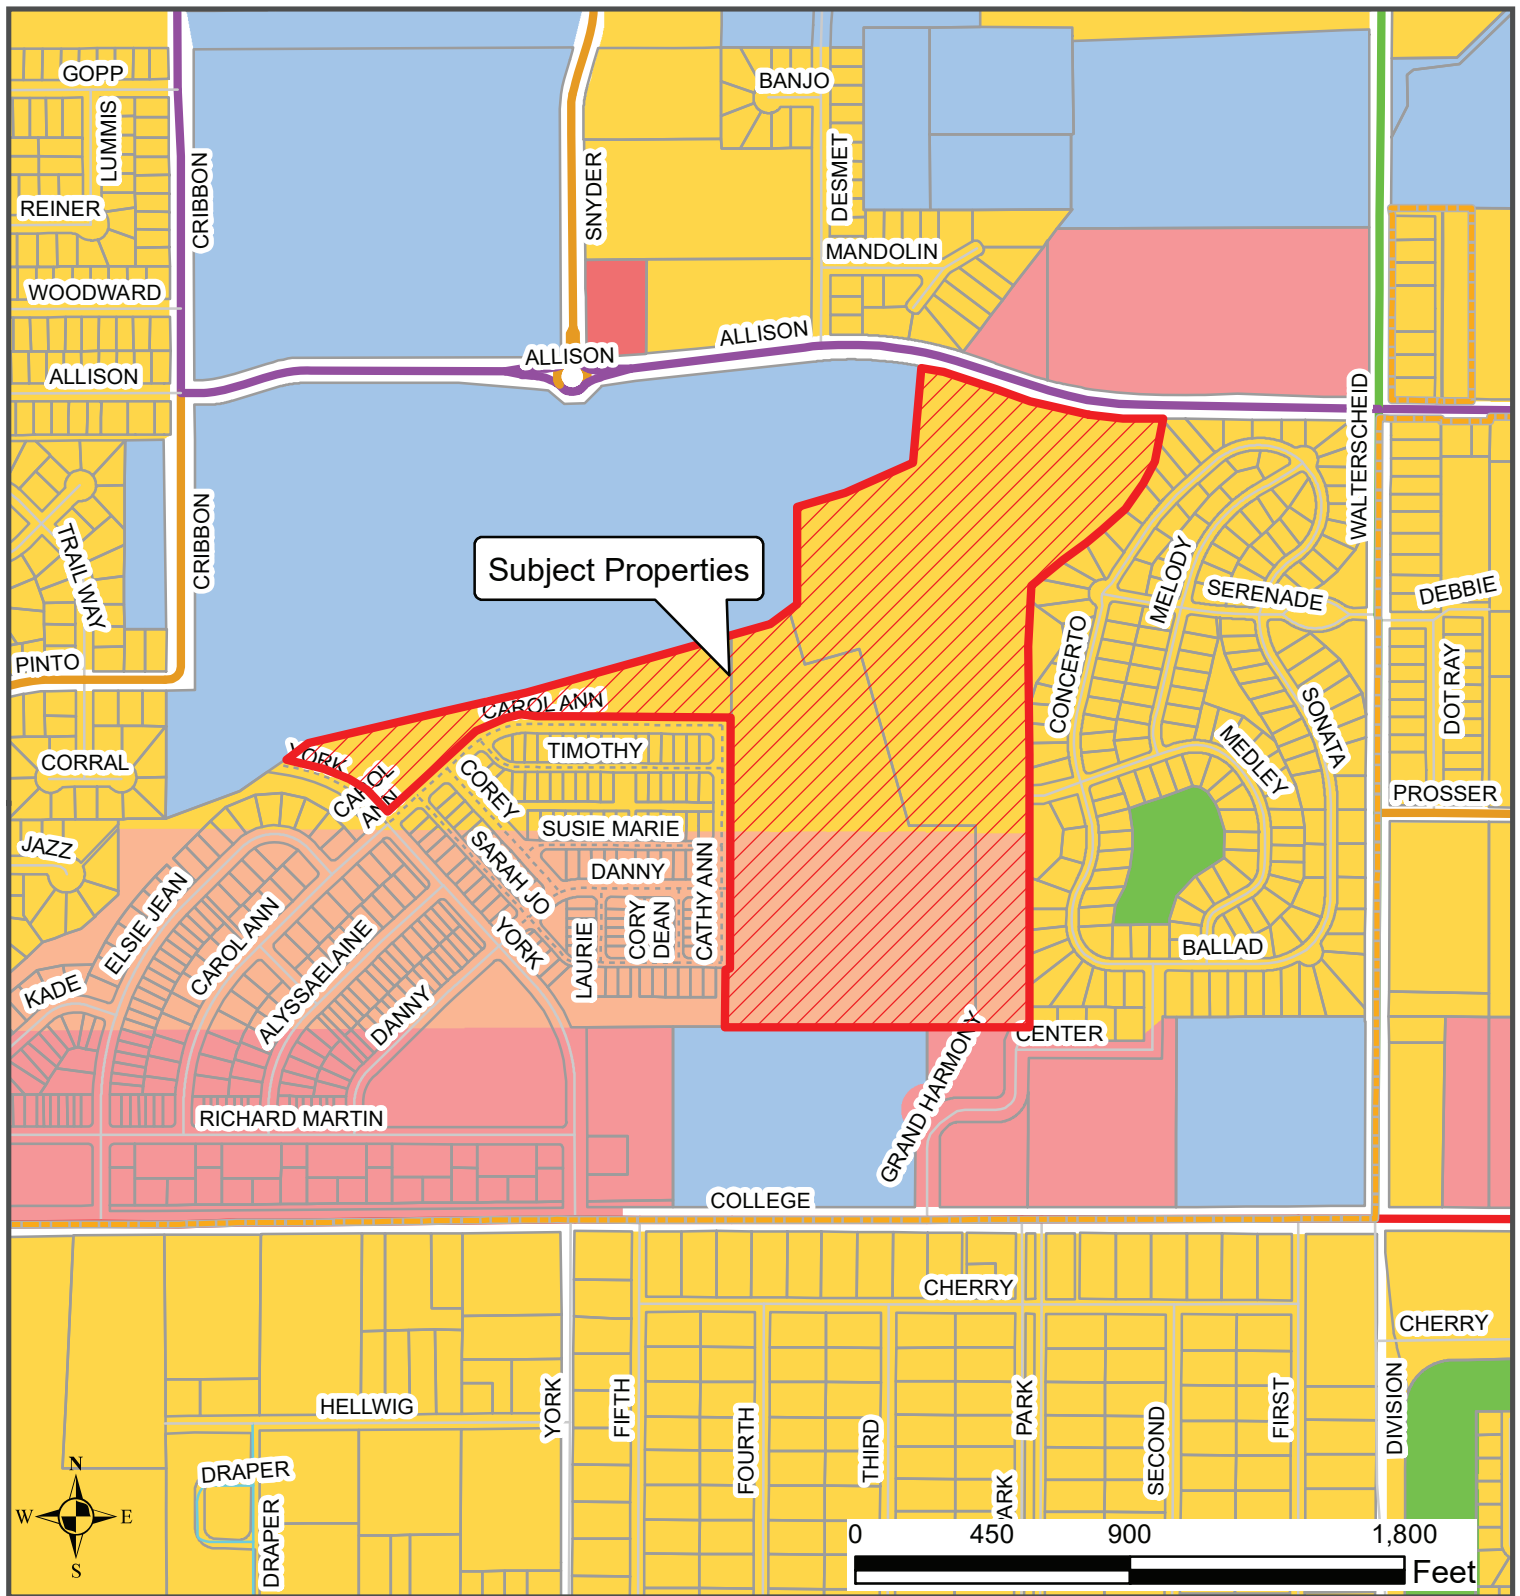

Attachment 2: Land Use Map PUDC-26-50

This map/data is made possible through the Cheyenne and Laramie County Cooperative GIS (CLCCGIS) Program and is for display purposes only. The CLCCGIS invokes its sovereign and governmental immunity in allowing access to or use of this data, makes no warranties as to the validity, and assumes no liability associated with the use or misuse of this information.

Legend

City Limits	Agricultural/Rural	Industrial
Interstate	Rural Residential	Central Business District
Principal Arterial	Urban Transition Residential	Community Business
Minor Arterial	Urban Residential	Public and Quasi-Public
Major Collector	Mixed-Use Residential	Military/Federal
Minor Collector	Mixed-Use Commercial	Open Space and Parks
Local	Mixed-Use Employment	
Private		
Platted not built		
Ownership		

**Record No: PUDC-
26-50**

Plat – Expedited

Status: Active

Submitted On: 3/9/2026

Primary Location

O CATHY ANN LN
Cheyenne, WY 82007

Owner

TRU GRIT LAND
DEVELOPMENT LLC
WALTERSCHEID BLVD 140
CHEYENNE, WY 82007-2370

Applicant

 John Sayers
 307-214-3093
 jsayers@mhbwy.com
 140 Walterscheid Blvd
Cheyenne, WY 82007

Application Information

This application has a deadline. The deadline is the second Wednesday of the month.
Application Schedule.

An expedited review is when both a preliminary and final plat are submitted to the Planning Commission together. To be eligible for expedited review the preliminary plat shall contain no significant planning, design, and engineering issues. Upon determination by staff, the applicant may submit a preliminary and final plat to the Planning Commission.*



I acknowledge the that Expedited status is not guaranteed.*



Written Statement* ?

We are proposing the next phase of the Harmony Valley Subdivision to include 196 residential units.

Project Name* ?

Harmony Valley 23rd Filing

Plat Title* ?

Harmony Valley 23rd Filing

Current Subdivision* ?

Harmony Valley 1st and 5th

Project area (acres)*

49.56

Proposed Lots* ?

196

Pre-application Meeting Date

02/11/2026

Park Fees are due at time of signing of the final plat mylar (see UDC 4.2.5). I acknowledge that this plat may be required to pay plat-level Park Fees.*



Public Improvements are required with platting actions. Please select the option that best demonstrates your intent for the public streets and other infrastructure adjacent to or within the plat boundary.*



Owner(s) (or developers) behind the plat application will construct the needed infrastructure.

Review Criteria

The following review criteria are found in the UDC regarding a Preliminary Plat. Please acknowledge the proposed plat meets each review criterion by checking the box.

The application is in accordance with the development policies and physical patterns identified in the Comprehensive Plan (2.1.2.d.1).*



The application reflects sound planning and urban design principles with respect to existing and potential future development in the vicinity, including consideration of current and future streets, open spaces, blocks and lots, and public utilities or facilities (2.1.2.d.2).*



The division of land meets the purposes, intent, and all applicable standards in Article 4 (2.1.2.d.3).*



Any phasing proposed in the application is clearly indicated and demonstrates a logical and wellplanned development pattern. This may include consideration of amenities and public facilities of the subdivision within each phase compared to the anticipated timing or the likelihood of future phases being constructed as planned (2.1.2.d.4).*



The impacts identified in specific studies or technical reports that were prepared or requested to be prepared in association with the application, and whether the findings and recommendations of these reports, or any modifications or conditions on approval of the application, can mitigate these impacts (2.1.2.d.5).*



Lots proposed for development shall be buildable lots according to the existing or proposed zoning district standards, result in site design and development patterns that meet the Intent and Applicability statements of the existing or proposed zoning district, and not aggravate nonconforming setbacks or currently adopted building and fire code access and separation requirements (2.1.2.d.6).*



All parcels not proposed as buildable lots and which are not dedicated to and accepted by the City shall have a clearly defined entity responsible for ongoing maintenance (2.1.2.d.7).*



The application will not create any undue influence on existing or potential development for adjacent property considering the existing zoning and Comprehensive Plan policies for that property (2.1.2.d.8).*



The application is not harmful to the public health, safety, and welfare (2.1.2.d.9).*



Remainder lot(s) shall be clearly identified on the preliminary plat and shall not be developed or proposed for development for purposes. Remainder lot(s) shall be noted and described on all plats either graphically or by legal description (2.1.2.d.10).*



The following review criteria are found in the UDC regarding a Final Plat. Please acknowledge the proposed plat meets each review criterion by checking the box.

The layout and design of the final plat is in substantial compliance with the approved preliminary plat considering the number of lots or parcels, street and block layout, and access, and any deviations in the final plat brings the application in further compliance with the Comprehensive Plan (2.1.3.d.1).*



The application meets any conditions or modifications of the approved preliminary plat (2.1.3.d.2). (Not applicable at time of application for an expedited plat)

The application meets the purposes, intent, and applicable standards of Article 4 (2.1.3.d.3).*




Certification

I hereby certify that I am the owner, applicant, or agent named herein and that I have familiarized myself with the rules and regulations with respect to the filing of this application and that the foregoing statements and answers contained on this application and accompanying documents are true and accurate to the best of my knowledge.*



John Sayers

Mar 9, 2026

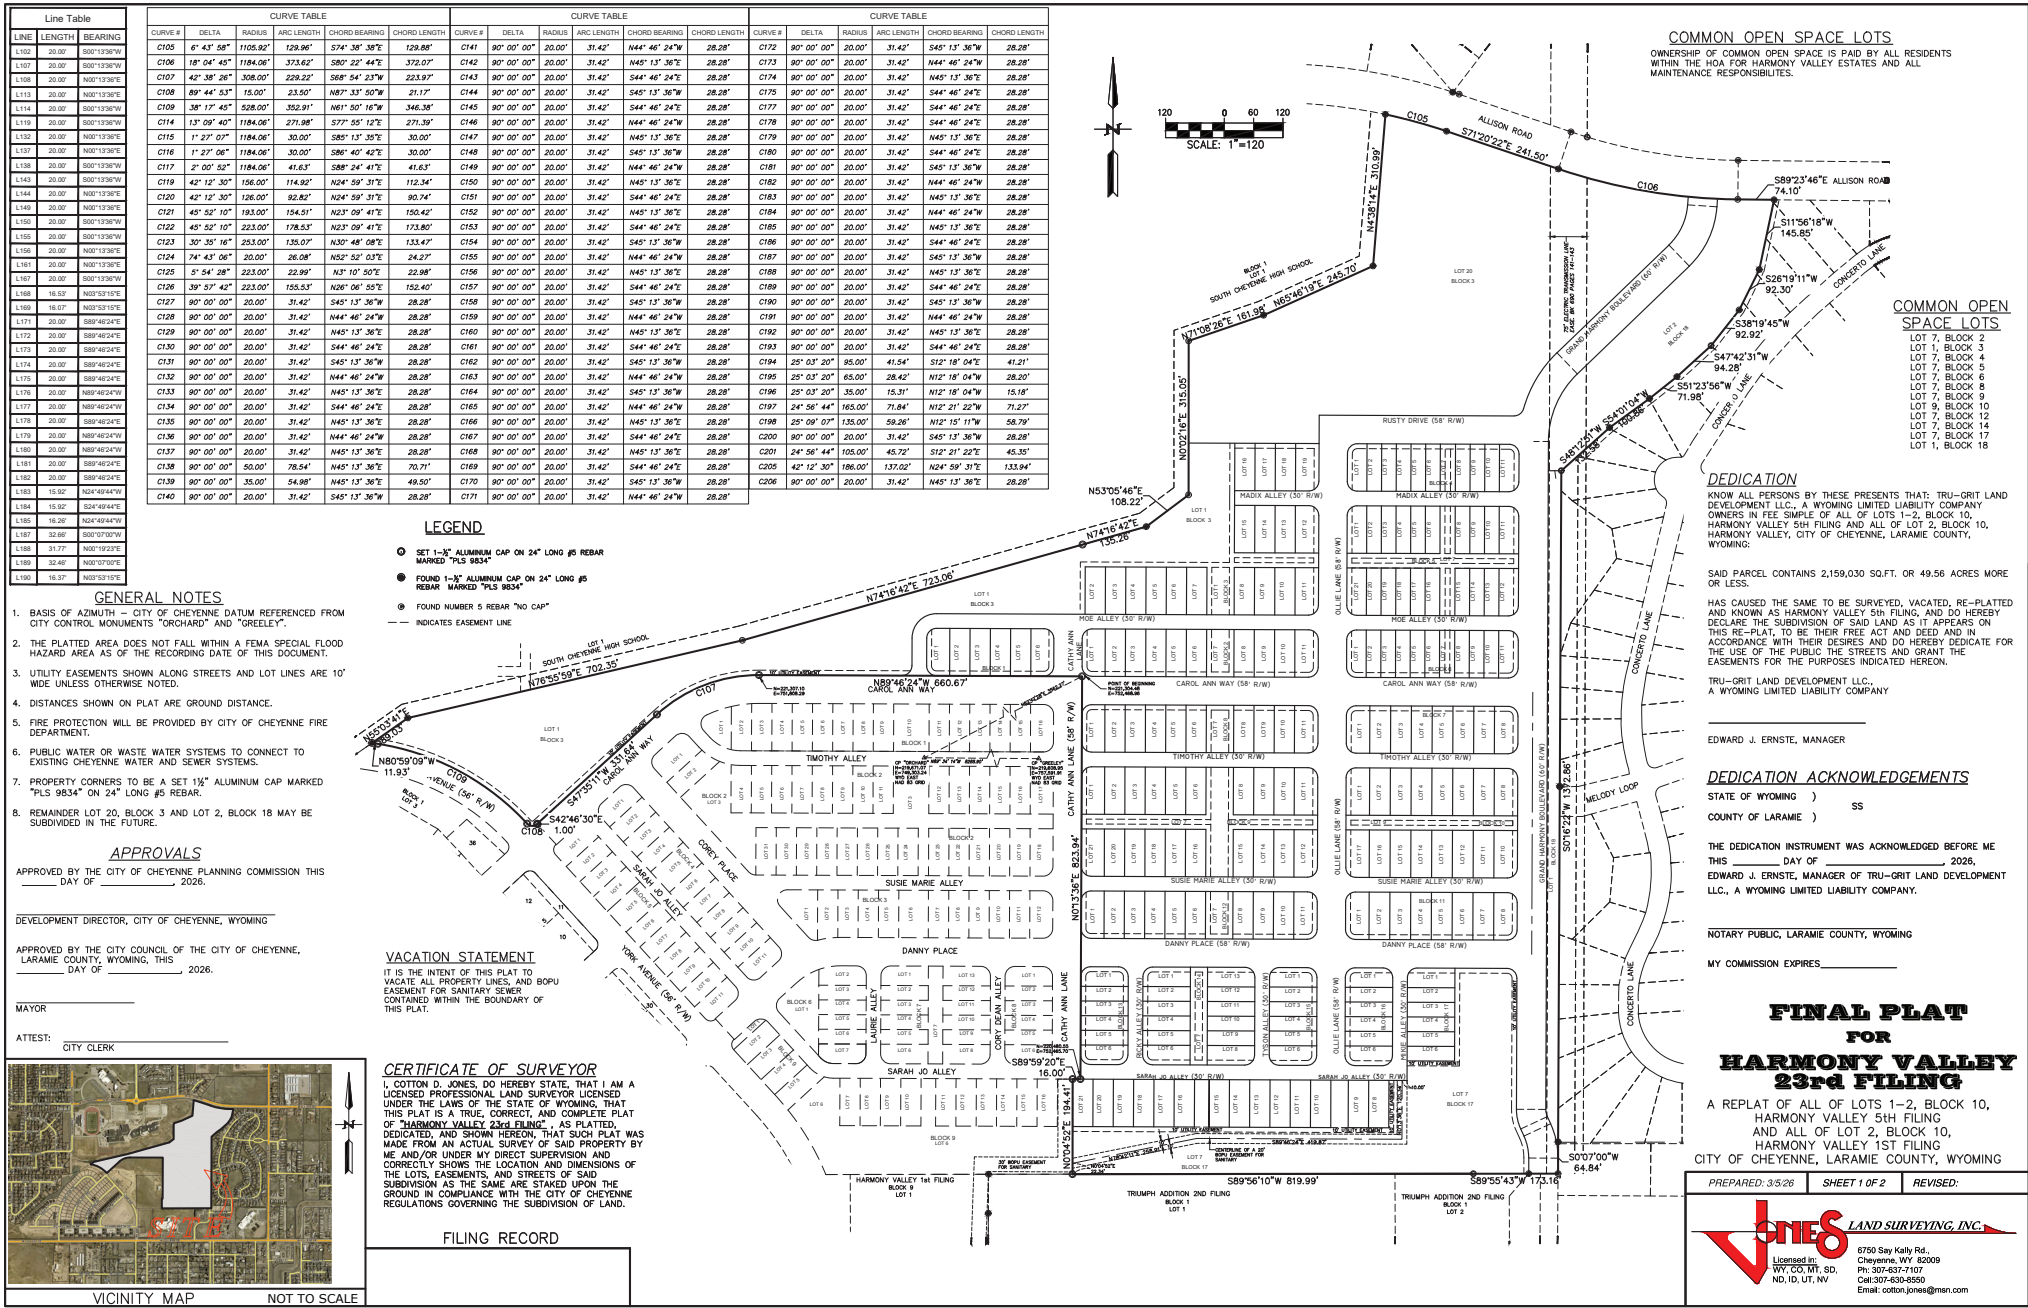


CURVE TABLE						CURVE TABLE						CURVE TABLE					
CURVE #	DELTA	RADIUS	ARC LENGTH	CHORD BEARING	CHORD LENGTH	CURVE #	DELTA	RADIUS	ARC LENGTH	CHORD BEARING	CHORD LENGTH	CURVE #	DELTA	RADIUS	ARC LENGTH	CHORD BEARING	CHORD LENGTH
C105	6° 43' 58"	1105.92	129.86	S74° 38' 39"E	129.86	C141	90° 00' 00"	20.00	31.42	N44° 46' 24"W	28.28	C172	90° 00' 00"	20.00	31.42	S45° 13' 36"E	28.28
C106	18° 04' 45"	1184.06	373.62	S80° 22' 44"E	373.62	C142	90° 00' 00"	20.00	31.42	N45° 13' 36"E	28.28	C173	90° 00' 00"	20.00	31.42	N44° 46' 24"W	28.28
C107	42° 38' 26"	308.00	229.22	S68° 54' 23"W	229.22	C143	90° 00' 00"	20.00	31.42	S44° 46' 24"W	28.28	C174	90° 00' 00"	20.00	31.42	N45° 13' 36"E	28.28
C108	89° 44' 53"	15.00	23.50	N87° 53' 50"W	21.17	C144	90° 00' 00"	20.00	31.42	S45° 13' 36"E	28.28	C175	90° 00' 00"	20.00	31.42	S44° 46' 24"E	28.28
C109	38° 17' 45"	528.00	352.91	N61° 50' 16"W	346.38	C145	90° 00' 00"	20.00	31.42	S44° 46' 24"E	28.28	C177	90° 00' 00"	20.00	31.42	S44° 46' 24"E	28.28
C114	13° 09' 40"	1184.06	271.98	S77° 55' 12"E	271.36	C146	90° 00' 00"	20.00	31.42	N44° 46' 24"W	28.28	C178	90° 00' 00"	20.00	31.42	S44° 46' 24"E	28.28
C115	1° 27' 06"	1184.06	30.00	S85° 13' 35"E	30.00	C147	90° 00' 00"	20.00	31.42	N45° 13' 36"E	28.28	C179	90° 00' 00"	20.00	31.42	N45° 13' 36"E	28.28
C116	1° 27' 06"	1184.06	30.00	S86° 40' 42"E	30.00	C148	90° 00' 00"	20.00	31.42	S45° 13' 36"W	28.28	C180	90° 00' 00"	20.00	31.42	S44° 46' 24"E	28.28
C117	2° 00' 52"	1184.06	41.63	S88° 54' 41"E	41.63	C149	90° 00' 00"	20.00	31.42	N44° 46' 24"W	28.28	C181	90° 00' 00"	20.00	31.42	S45° 13' 36"W	28.28
C119	42° 12' 30"	156.00	114.92	N24° 59' 31"E	112.34	C150	90° 00' 00"	20.00	31.42	N45° 13' 36"E	28.28	C182	90° 00' 00"	20.00	31.42	N44° 46' 24"W	28.28
C120	42° 12' 30"	126.00	92.62	N24° 59' 31"E	90.74	C151	90° 00' 00"	20.00	31.42	S44° 46' 24"E	28.28	C183	90° 00' 00"	20.00	31.42	N45° 13' 36"E	28.28
C121	45° 52' 10"	193.00	154.51	N23° 09' 41"E	150.42	C152	90° 00' 00"	20.00	31.42	N45° 13' 36"E	28.28	C184	90° 00' 00"	20.00	31.42	N44° 46' 24"W	28.28
C122	45° 52' 10"	223.00	178.53	N23° 09' 41"E	173.80	C153	90° 00' 00"	20.00	31.42	S44° 46' 24"E	28.28	C185	90° 00' 00"	20.00	31.42	N45° 13' 36"E	28.28
C123	30° 35' 16"	253.00	150.07	N30° 46' 09"E	133.47	C154	90° 00' 00"	20.00	31.42	S45° 13' 36"W	28.28	C186	90° 00' 00"	20.00	31.42	S44° 46' 24"E	28.28
C124	74° 43' 08"	20.00	26.06	N52° 52' 03"E	24.27	C155	90° 00' 00"	20.00	31.42	N44° 46' 24"W	28.28	C187	90° 00' 00"	20.00	31.42	S45° 13' 36"W	28.28
C125	5° 54' 28"	233.00	23.99	N3° 10' 50"E	23.98	C156	90° 00' 00"	20.00	31.42	N45° 13' 36"E	28.28	C188	90° 00' 00"	20.00	31.42	N45° 13' 36"E	28.28
C126	39° 53' 42"	233.00	155.53	N26° 06' 55"E	152.40	C157	90° 00' 00"	20.00	31.42	S44° 46' 24"E	28.28	C189	90° 00' 00"	20.00	31.42	S44° 46' 24"E	28.28
C127	90° 00' 00"	20.00	31.42	S45° 13' 36"W	28.28	C158	90° 00' 00"	20.00	31.42	S45° 13' 36"W	28.28	C190	90° 00' 00"	20.00	31.42	S45° 13' 36"W	28.28
C128	90° 00' 00"	20.00	31.42	N44° 46' 24"W	28.28	C159	90° 00' 00"	20.00	31.42	N44° 46' 24"W	28.28	C191	90° 00' 00"	20.00	31.42	N44° 46' 24"W	28.28
C129	90° 00' 00"	20.00	31.42	N45° 13' 36"E	28.28	C160	90° 00' 00"	20.00	31.42	N45° 13' 36"E	28.28	C192	90° 00' 00"	20.00	31.42	N45° 13' 36"E	28.28
C130	90° 00' 00"	20.00	31.42	S44° 46' 24"W	28.28	C161	90° 00' 00"	20.00	31.42	S44° 46' 24"W	28.28	C193	90° 00' 00"	20.00	31.42	S44° 46' 24"W	28.28
C131	90° 00' 00"	20.00	31.42	S45° 13' 36"W	28.28	C162	90° 00' 00"	20.00	31.42	S45° 13' 36"W	28.28	C194	25° 03' 20"	95.00	41.54	S12° 18' 04"E	41.21
C132	90° 00' 00"	20.00	31.42	N44° 46' 24"W	28.28	C163	90° 00' 00"	20.00	31.42	N44° 46' 24"W	28.28	C195	25° 03' 20"	65.00	28.42	N12° 18' 04"W	28.20
C133	90° 00' 00"	20.00	31.42	N45° 13' 36"E	28.28	C164	90° 00' 00"	20.00	31.42	S45° 13' 36"W	28.28	C196	25° 03' 20"	35.00	15.31	N12° 18' 04"W	15.18
C134	90° 00' 00"	20.00	31.42	S44° 46' 24"E	28.28	C165	90° 00' 00"	20.00	31.42	N44° 46' 24"W	28.28	C197	24° 56' 44"	163.00	71.84	N12° 21' 22"W	71.27
C135	90° 00' 00"	20.00	31.42	N45° 13' 36"E	28.28	C166	90° 00' 00"	20.00	31.42	N45° 13' 36"E	28.28	C198	25° 09' 07"	135.00	58.26	N12° 15' 11"W	58.79
C136	90° 00' 00"	20.00	31.42	N44° 46' 24"W	28.28	C167	90° 00' 00"	20.00	31.42	S44° 46' 24"W	28.28	C200	90° 00' 00"	20.00	31.42	S45° 13' 36"W	28.28
C137	90° 00' 00"	20.00	31.42	N45° 13' 36"E	28.28	C168	90° 00' 00"	20.00	31.42	N45° 13' 36"E	28.28	C201	24° 56' 44"	105.00	45.72	S12° 21' 22"E	45.35
C138	90° 00' 00"	50.00	78.54	N45° 13' 36"E	70.71	C169	90° 00' 00"	20.00	31.42	S44° 46' 24"E	28.28	C205	42° 12' 30"	186.00	137.02	N24° 59' 31"E	133.94
C139	90° 00' 00"	35.00	54.98	N45° 13' 36"E	49.50	C170	90° 00' 00"	20.00	31.42	S45° 13' 36"W	28.28	C206	90° 00' 00"	20.00	31.42	N45° 13' 36"E	28.28
C140	90° 00' 00"	20.00	31.42	S45° 13' 36"W	28.28	C171	90° 00' 00"	20.00	31.42	N44° 46' 24"W	28.28						

VACATION STATEMENT


IT IS THE INTENT OF THIS PLAT TO VACATE ALL PROPERTY LINES, AND BOPU EASEMENT FOR SANITARY SEWER CONTAINED WITHIN THE BOUNDARY OF THIS PLAT.

FILING RECORD

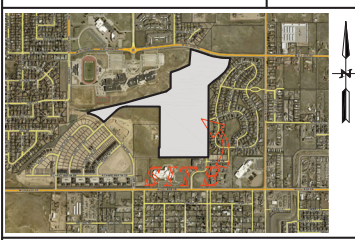

VICINITY MAP NOT TO SCALE

[c:\projects\harmony_valley_23rd_filing\coord\09-10-23rd_filing_scale_100.mxd | 4/21/2026 12:02 PM]

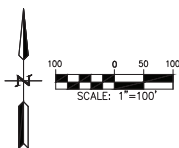

COMMON OPEN SPACE LOTS

OWNERSHIP OF COMMON OPEN SPACE IS PAID BY ALL RESIDENTS WITHIN THE HOA FOR HARMONY VALLEY ESTATES AND ALL MAINTENANCE RESPONSIBILITIES.

Line	LENGTH	BEARING
L102	20.00	S00°13'30"W
L107	20.00	S00°13'30"W
L108	20.00	S00°13'30"E
L113	20.00	N00°13'30"E
L114	20.00	S00°13'30"W
L115	20.00	S00°13'30"W
L132	20.00	N00°13'30"E
L137	20.00	N00°13'30"E
L138	20.00	N00°13'30"W
L143	20.00	S00°13'30"W
L144	20.00	N00°13'30"E
L149	20.00	S00°13'30"W
L150	20.00	S00°13'30"W
L155	20.00	S00°13'30"W
L156	20.00	N00°13'30"E
L167	20.00	N00°13'30"E
L168	16.37	N00°13'30"E
L169	16.37	N00°13'30"E
L171	20.00	S00°13'30"E
L172	20.00	S00°13'30"E
L173	20.00	S00°13'30"E
L174	20.00	S00°13'30"E
L175	20.00	S00°13'30"E
L176	20.00	S00°13'30"E
L177	20.00	S00°13'30"E
L178	20.00	S00°13'30"E
L179	20.00	S00°13'30"E
L180	20.00	S00°13'30"E
L181	20.00	S00°13'30"E
L182	20.00	S00°13'30"E
L183	15.92	S04°46'24"E
L184	15.92	S04°46'24"E
L185	16.29	S04°46'24"E
L187	32.80	S00°13'30"W
L188	31.77	N00°13'30"W
L189	32.48	N00°13'30"E
L190	16.37	N00°13'30"E

COMMON OPEN SPACE LOTS

- LOT 7, BLOCK 2
- LOT 1, BLOCK 3
- LOT 7, BLOCK 4
- LOT 7, BLOCK 5
- LOT 7, BLOCK 6
- LOT 7, BLOCK 8
- LOT 7, BLOCK 9
- LOT 9, BLOCK 10
- LOT 7, BLOCK 12
- LOT 7, BLOCK 14
- LOT 1, BLOCK 18

LEGEND

- SET 1-1/2" ALUMINUM CAP ON 24" LONG #5 REBAR MARKED "PLS 9834"
- FOUND 1-1/2" ALUMINUM CAP ON 24" LONG #5 REBAR MARKED "PLS 9834"
- FOUND NUMBER 5 REBAR "NO CAP"
- - - INDICATES EASEMENT LINE

GENERAL NOTES

1. BASIS OF AZIMUTH - CITY OF CHEYENNE DATUM REFERENCED FROM CITY CONTROL MONUMENTS "ORCHARD" AND "GORELLEY".
2. THE PLATTED AREA DOES NOT FALL WITHIN A FEMA SPECIAL FLOOD HAZARD AREA AS OF THE RECORDING DATE OF THIS DOCUMENT.
3. UTILITY EASEMENTS SHOWN ALONG STREETS AND LOT LINES ARE 10' WIDE UNLESS OTHERWISE NOTED.
4. DISTANCES SHOWN ON PLAT ARE GROUND DISTANCE.
5. FIRE PROTECTION WILL BE PROVIDED BY CITY OF CHEYENNE FIRE DEPARTMENT.
6. PUBLIC WATER OR WASTE WATER SYSTEMS TO CONNECT TO EXISTING CHEYENNE WATER AND SEWER SYSTEMS.
7. PROPERTY CORNERS TO BE A SET 1 1/2" ALUMINUM CAP MARKED "PLS 9834" ON 24" LONG #5 REBAR.
8. REMAINDER LOT 20, BLOCK 3 AND LOT 2, BLOCK 18 WILL BE SUBDIVIDED IN THE FUTURE.

FINAL PLAT FOR HARMONY VALLEY 23rd FILING

A REPLAT OF ALL OF LOTS 1-2, BLOCK 10, HARMONY VALLEY 5TH FILING AND ALL OF LOT 2, BLOCK 10, HARMONY VALLEY 1ST FILING CITY OF CHEYENNE, LARAMIE COUNTY, WYOMING

PREPARED: 3/5/26 SHEET 2 OF 2 REVISED:

